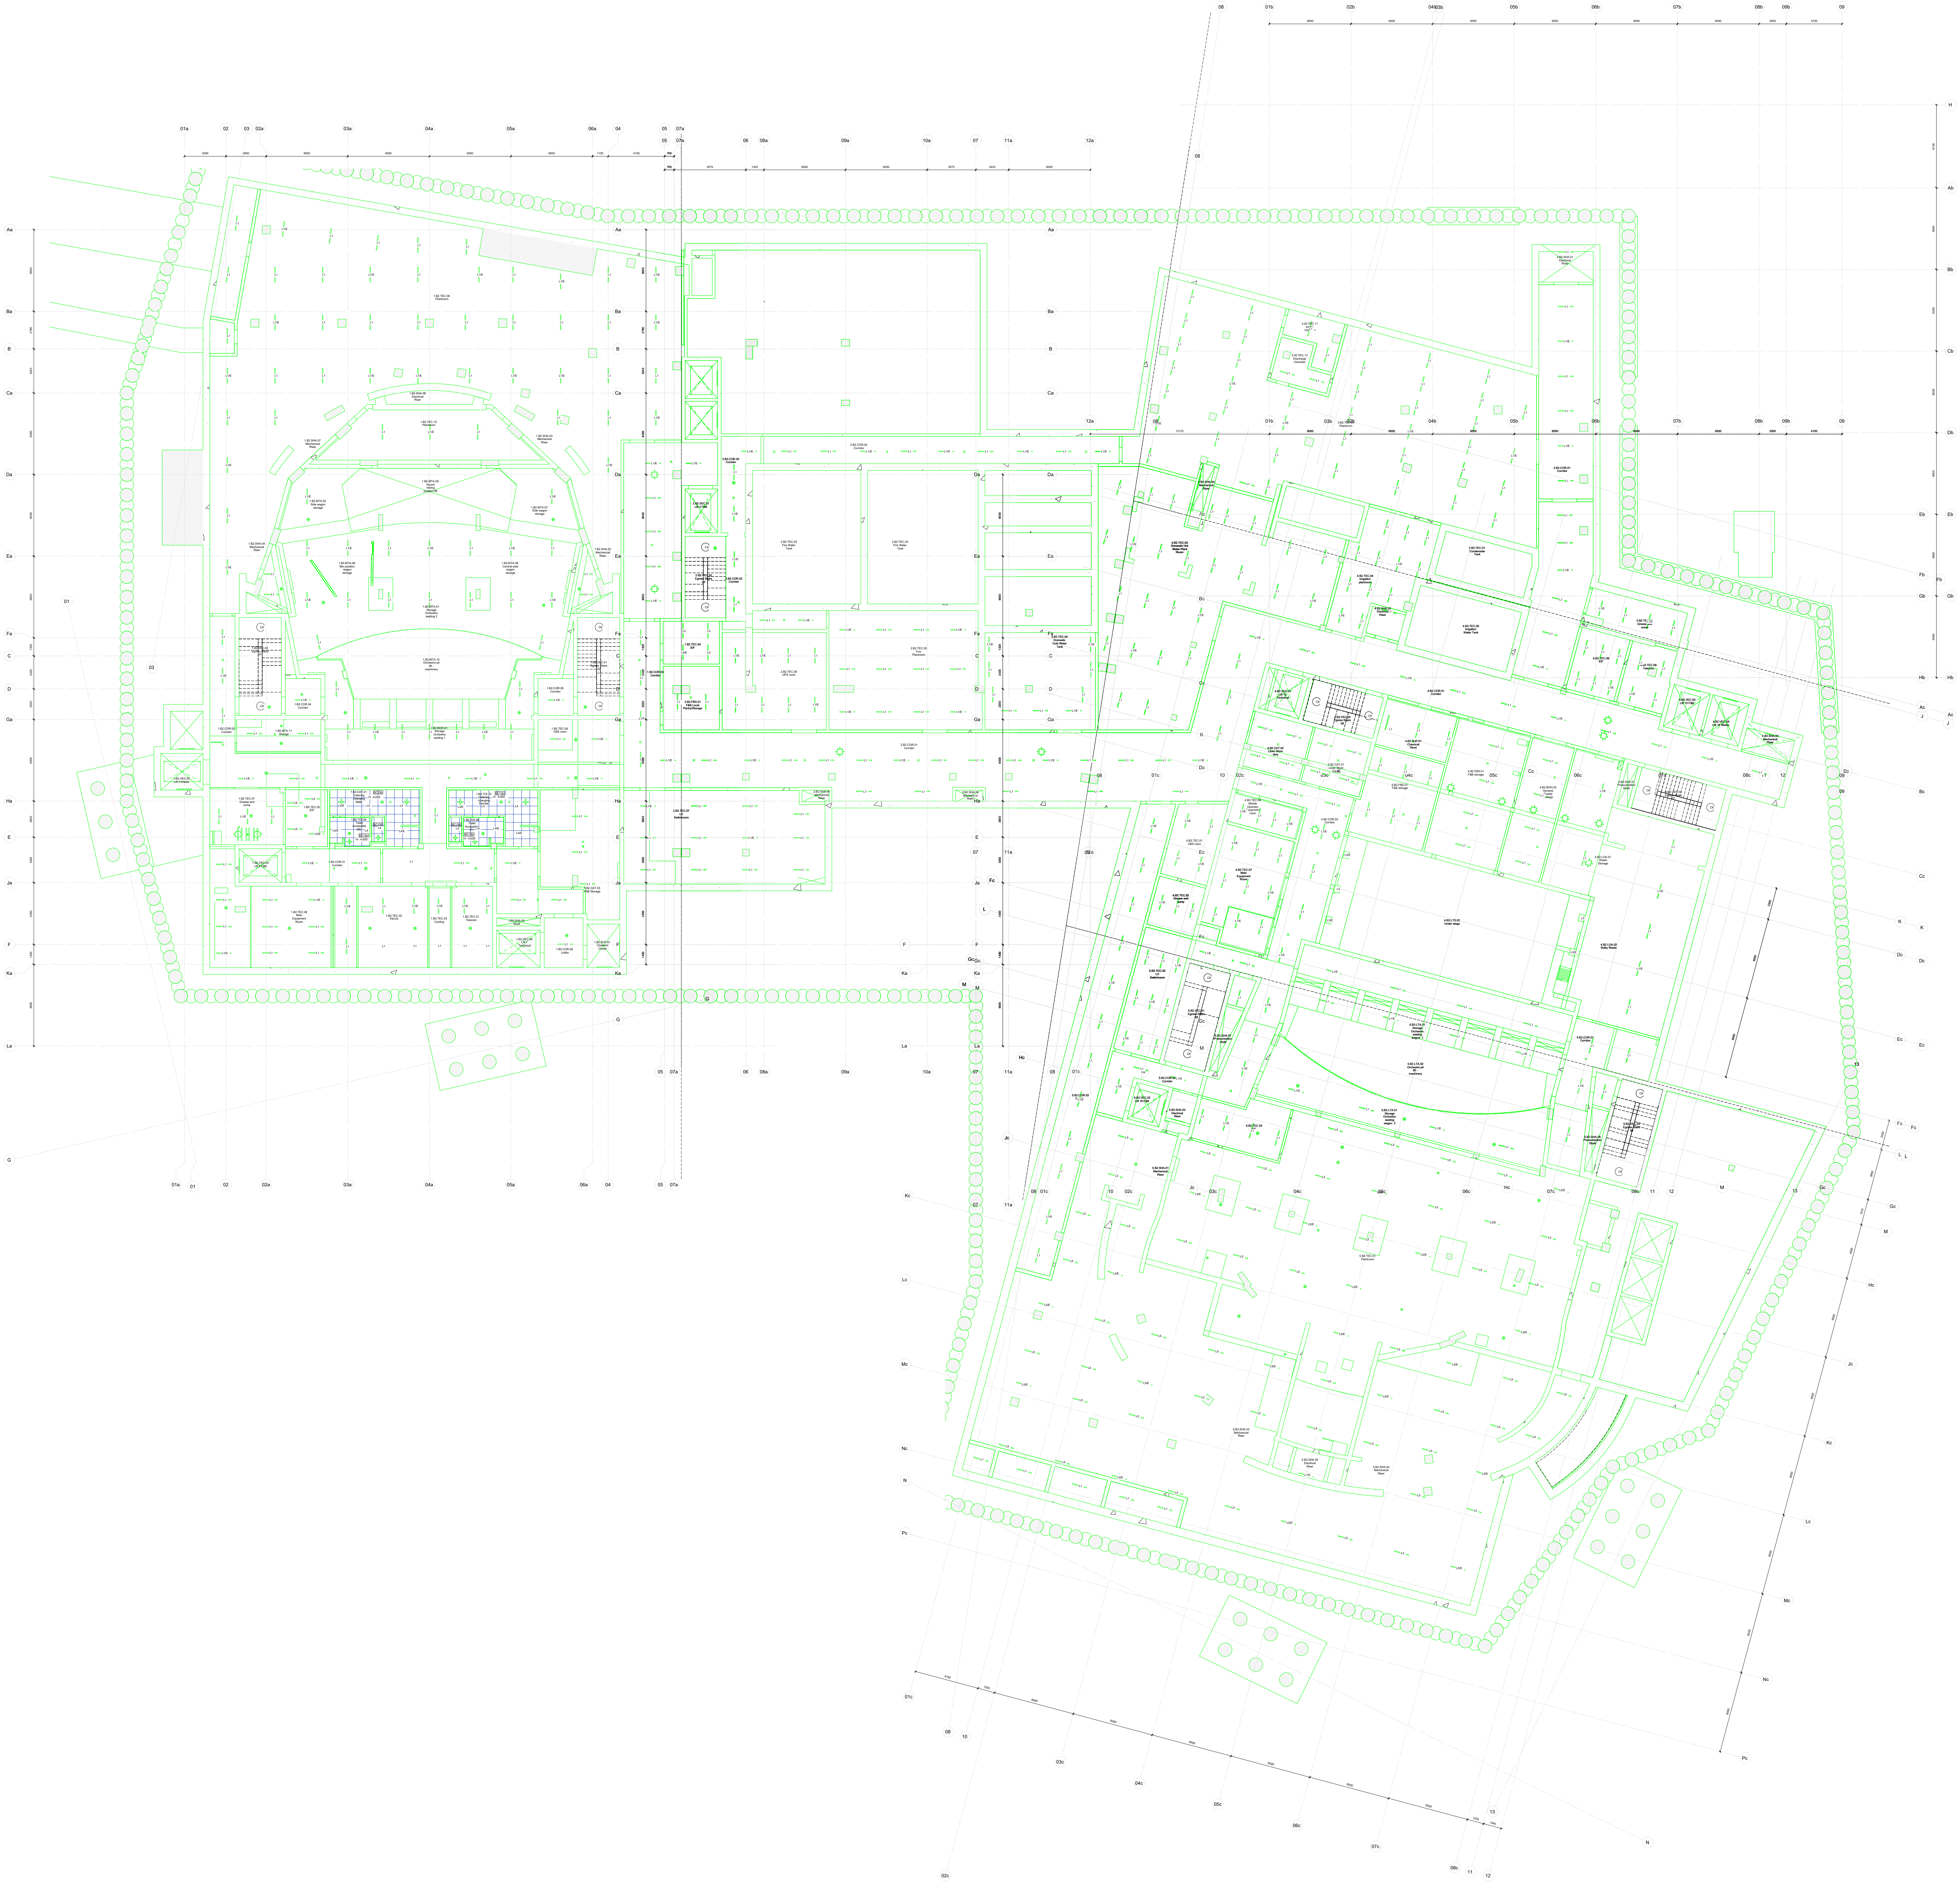

CEILING SYMBOLS

H: X,XXX CEILING HEIGHT, PROJECT BASE POINT

—	SIGNAGE - HANGING JUNCTION
•	SPRINKLER
○	SMOKE DETECTOR
✳	FIRE ALARM SOUNDER
¤	INFRARED SWITCH
⤢	ACCESS HATCH
□ ○ ▭	AIR DIFFUSER - SUPPLY
□ ○ ▭	AIR DIFFUSER - RETURN

FOR OTHER SYMBOLS LEGEND REFER TO DOCUMENTS:
JOH-BHC-S4-01-056-ZZZ-XX-DR-ME-010020
JOH-BHC-S4-01-056-ZZZ-XX-DR-EL-010020
JOH-BHC-S4-01-056-ZZZ-XX-DR-PH-010020

LIGHTING FIXTURES

⊠	Ceiling recessed (Type A1, A2)
⊠	Ceiling recessed (Type A3)
⊠	Ceiling recessed (Type A4, A7)
▭	Ceiling recessed (Type A5, A6, A19)
⊠	Ceiling recessed (Type A8, A11, A13, A17)
⊗	Ceiling recessed (Type A9)
⊠	Ceiling recessed (Type A10)
⊠	Ceiling recessed (Type A12)
▭	Ceiling recessed (Type A14)
·	Ceiling recessed (Type A15)
·	Ceiling recessed (Type A16)
⊠	Ceiling recessed (Type A16)
—	Ceiling recessed in profile (Type B1)
—	Ceiling mounted (Type C1.1, C2.1, C9.1, C10.1)
—	Ceiling mounted (Type C1.2, C2.2, C9.2, C10.2)
—	Ceiling mounted (Type C1.3, C2.3, C9.3, C10.3)
—	Ceiling mounted (Type C3.1)
—	Ceiling mounted (Type C3.2)
—	Ceiling mounted (Type C3.3)
—	Ceiling mounted (Type C4.1)
—	Ceiling mounted (Type C4.2)
—	Ceiling mounted (Type C4.3)
○	Ceiling mounted (Type C5)
—	Ceiling mounted (Type C6.1)
—	Ceiling mounted (Type C6.2)
—	Ceiling mounted (Type C6.3)
○	Ceiling mounted (Type C7)
○	Ceiling mounted (Type C8)
○	Ceiling mounted (Type C11)
—	Ceiling mounted (Type C12)
—	Ceiling mounted (Type C13)
○	Pendant, bespoke (Type D1)
⊗	Pendant, bespoke (Type D2)
⊗	Pendant, bespoke (Type D3)
⊗	Pendant (Type D5)
•	Track mounted (Type F1)
▭	Track mounted (Type F2)
═	Track (Type G1)

FOR LIGHTING FIXTURE SCHEDULE AND SPECIFICATION
REFER TO DOCUMENT:
JOH-HLA-S4-01-056-XXX-DS-DSR-YL-000027

CEILING SYMBOLS
H: X,XXX CEILING HEIGHT, PROJECT BASE POINT
SIGNAGE - HANGING JUNCTION
SPRINKLER
SMOKE DETECTOR
FIRE ALARM SOUNDER
INFRARED SWITCH
ACCESS HATCH
AIR DIFFUSER - SUPPLY
AIR DIFFUSER - RETURN
FOR OTHER SYMBOLS LEGEND REFER TO DOCUMENTS:
JOH-BHC-S4-01-056-ZZZ-XX-DR-ME-010020
JOH-BHC-S4-01-056-ZZZ-XX-DR-EL-010020
JOH-BHC-S4-01-056-ZZZ-XX-DR-PH-010020
LIGHTING FIXTURES
Ceiling recessed (Type A1, A2)
Ceiling recessed (Type A3)
Ceiling recessed (Type A4, A7)
Ceiling recessed (Type A5, A6, A19)
Ceiling recessed (Type A8, A11, A13, A17)
Ceiling recessed (Type A9)
Ceiling recessed (Type A10)
Ceiling recessed (Type A12)
Ceiling recessed (Type A14)
Ceiling recessed (Type A15)
Ceiling recessed (Type A16)
Ceiling recessed (Type A16)
Ceiling recessed in profile (Type B1)
Ceiling mounted (Type C1.1, C2.1, C9.1, C10.1)
Ceiling mounted (Type C1.2, C2.2, C9.2, C10.2)
Ceiling mounted (Type C1.3, C2.3, C9.3, C10.3)
Ceiling mounted (Type C3.1)
Ceiling mounted (Type C3.2)
Ceiling mounted (Type C3.3)
Ceiling mounted (Type C4.1)
Ceiling mounted (Type C4.2)
Ceiling mounted (Type C4.3)
Ceiling mounted (Type C5)
Ceiling mounted (Type C6.1)
Ceiling mounted (Type C6.2)
Ceiling mounted (Type C6.3)
Ceiling mounted (Type C7)
Ceiling mounted (Type C8)
Ceiling mounted (Type C11)
Ceiling mounted (Type C12)
Ceiling mounted (Type C13)
Pendant, bespoke (Type D1)
Pendant, bespoke (Type D2)
Pendant, bespoke (Type D3)
Pendant (Type D5)
Track mounted (Type F1)
Track mounted (Type F2)
Track (Type G1)
FOR LIGHTING FIXTURE SCHEDULE AND SPECIFICATION
REFER TO DOCUMENT:
JOH-HLA-S4-01-056-XXX-DS-DSR-YL-000027